CLEANING SCHEDULE


6 Days (Sunday-Friday)

5 Days (Sunday-Thursday)

APPA LEVEL ONE STANDARD

ALL OTHER AREAS TO BE CLEANED WILL BE LEVEL TWO

NO CLEANING IN THESE AREAS

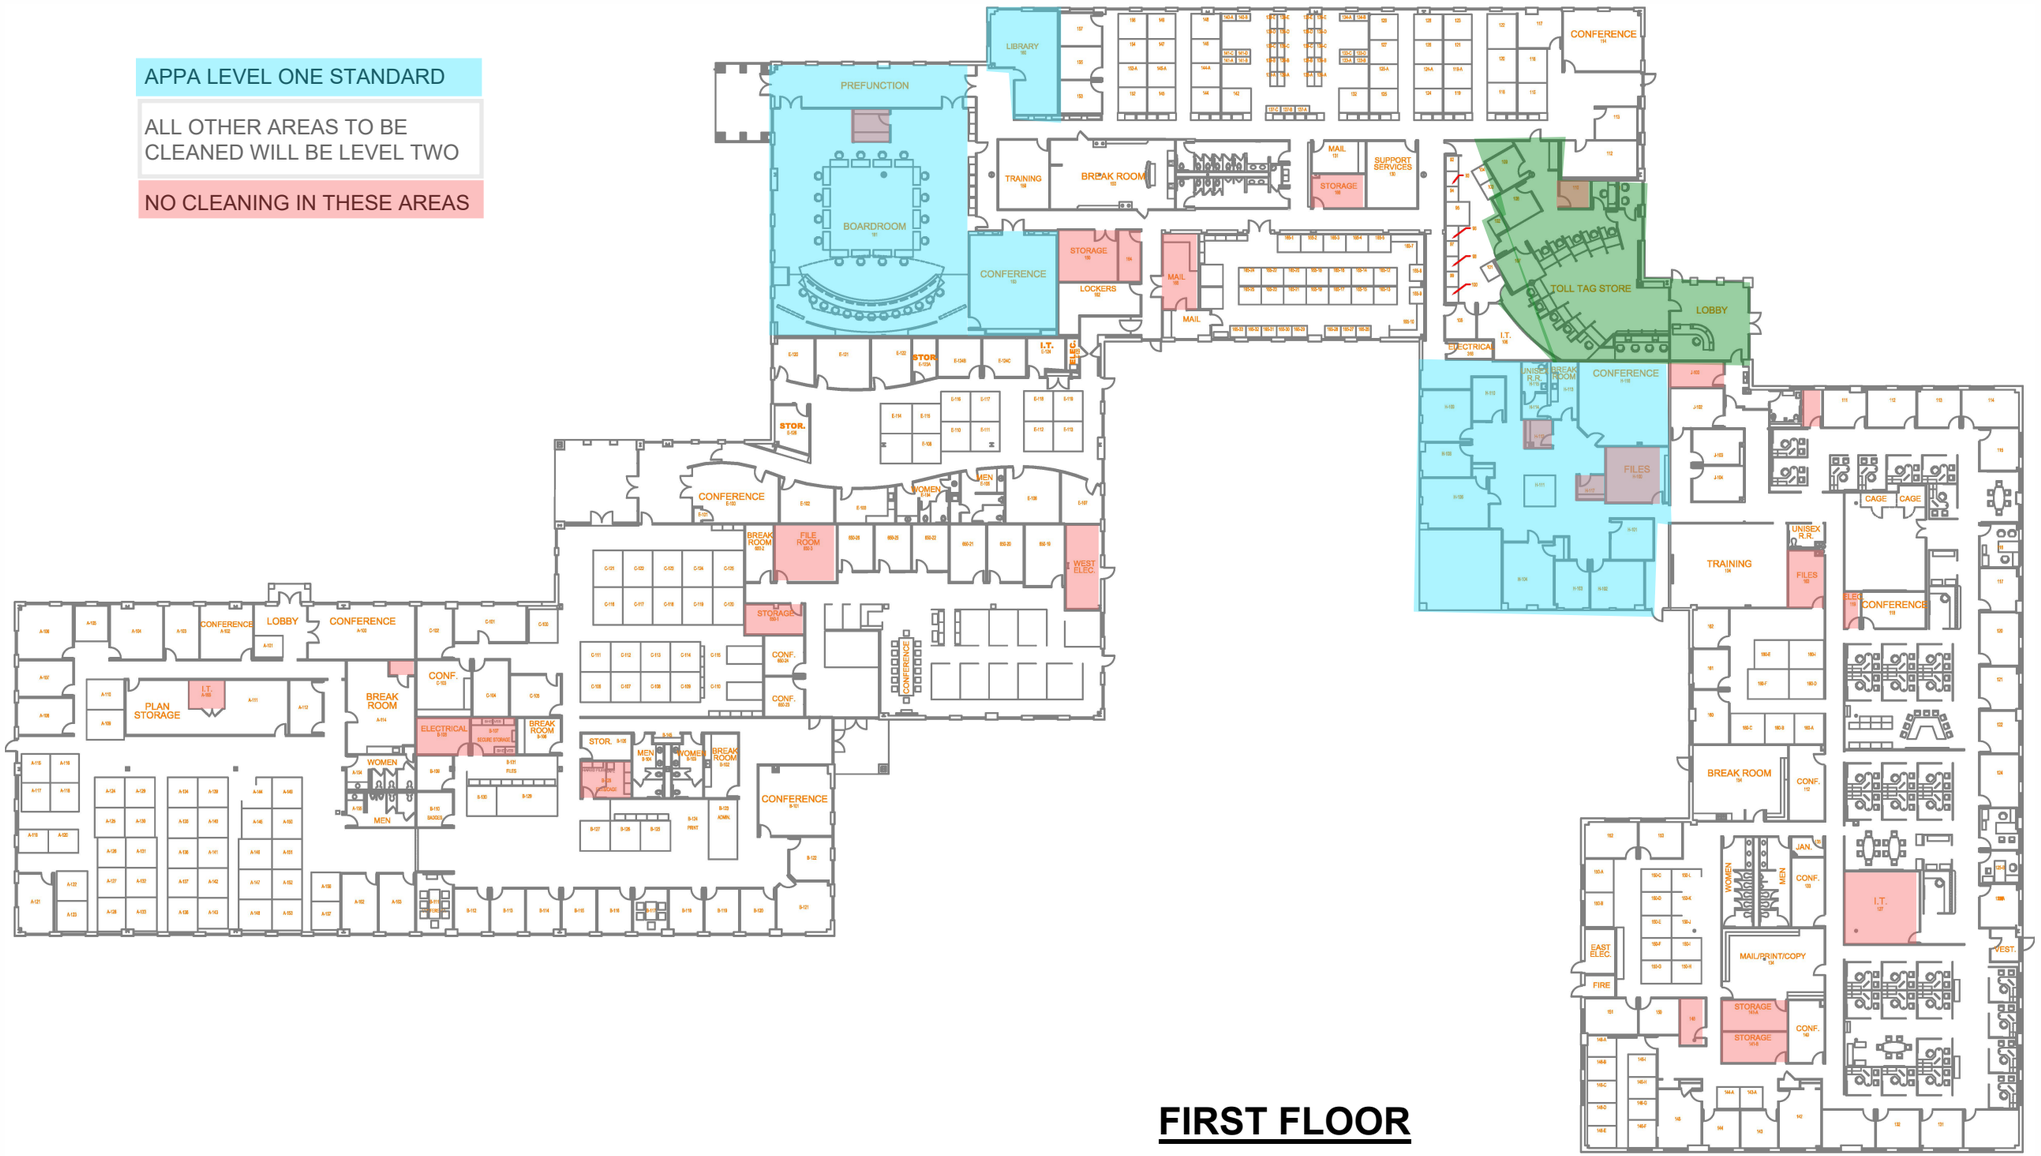

FIRST FLOOR

5900 W. PLANO PARKWAY

5910 W. PLANO PARKWAY

APPA LEVEL ONE STANDARD


ALL OTHER AREAS TO BE CLEANED WILL BE LEVEL TWO

NO CLEANING IN THESE AREAS

6 Days (Sunday-Friday)



SECOND FLOOR

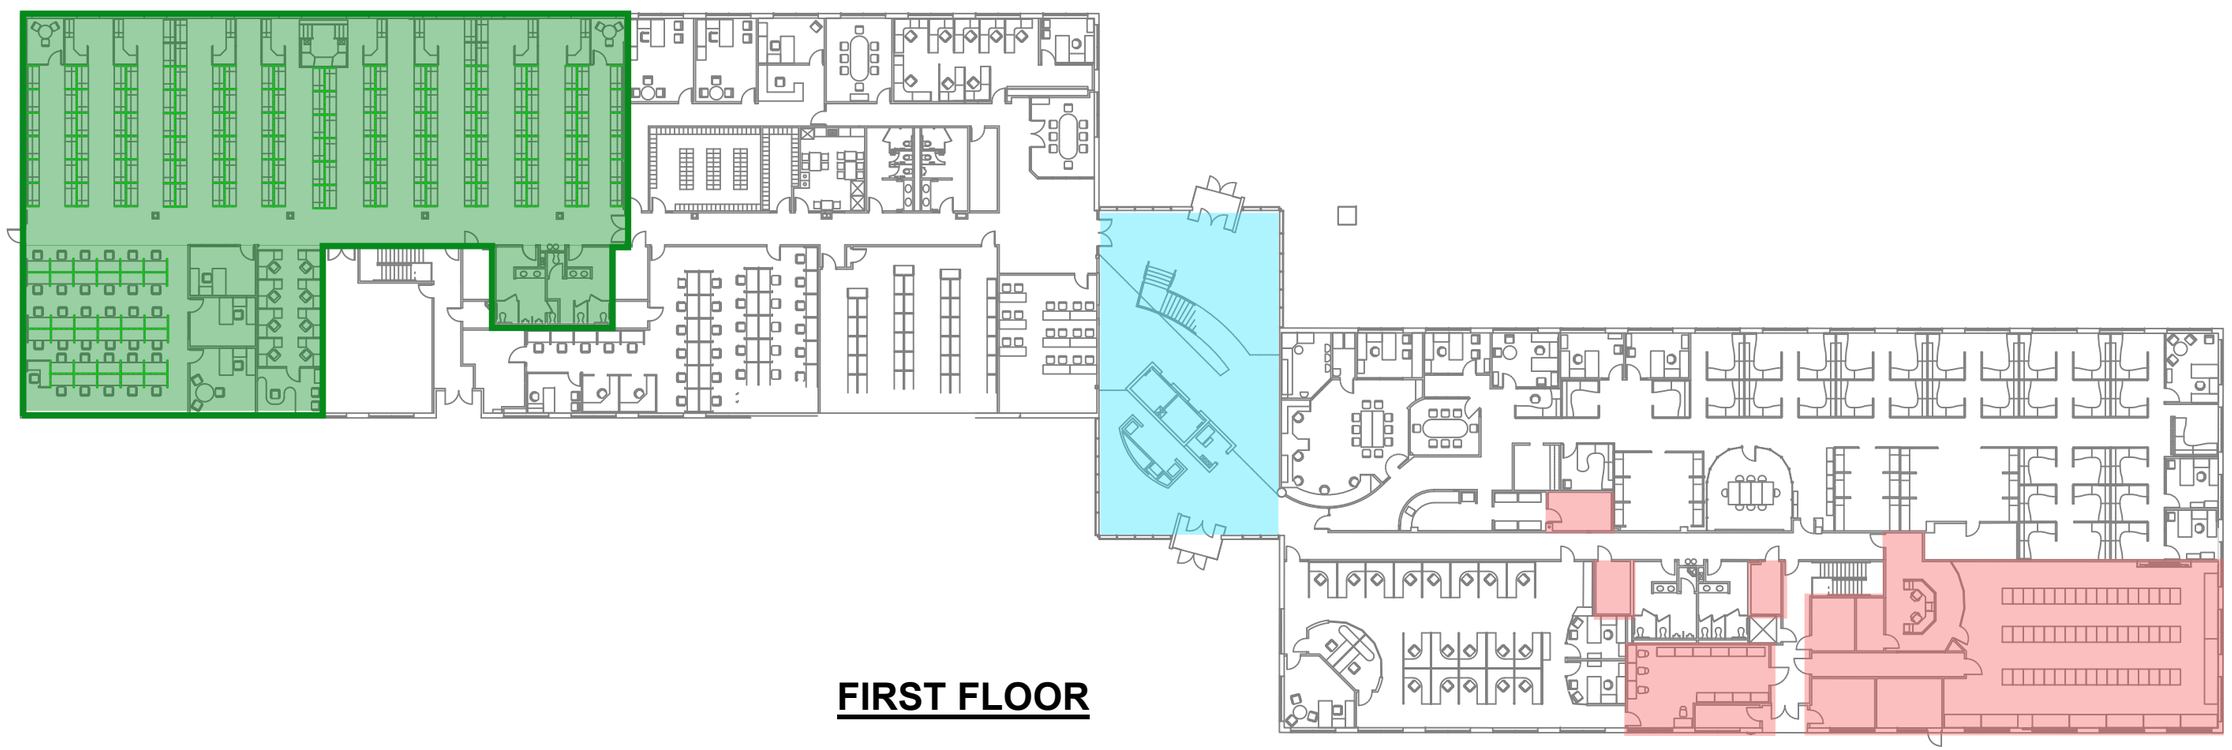

FIRST FLOOR